

Keynote - Kælder

Type nr. Opbygning

213001	Kældervæg (MU) 25 mm puds (MU) 100 mm isolat (MU) 250 mm isolering (BE) Bagmur af beton jf. KON-projekt
328001	Trædnethvæg (TØ) 50 mm trænet

BIL - PARKERINGSOPGØRELSE

I PROJEKTET

Bil 2.3 x 5.0 m

22

Bil 2.5 x 5.0 m

104

Bil. Handicapa 2.5 x 5.0 m

6

ALT

132

CYKEL - PARKERINGSOPGØRELSE

Ovel Kælder

500

Ovel Terræn

xxx??

I ALT

xx??

DEPOTER

I PROJEKTET

Depot

295

N

CF

CG

CH

CL

CA

CJ

CI

DK

DD

DC

DB

DA

DH

DI

VAG

DK


DE

DD


DA

DK

WALLS & COLUMNS IN STUE SLAB & BEAM ABOVE STUE

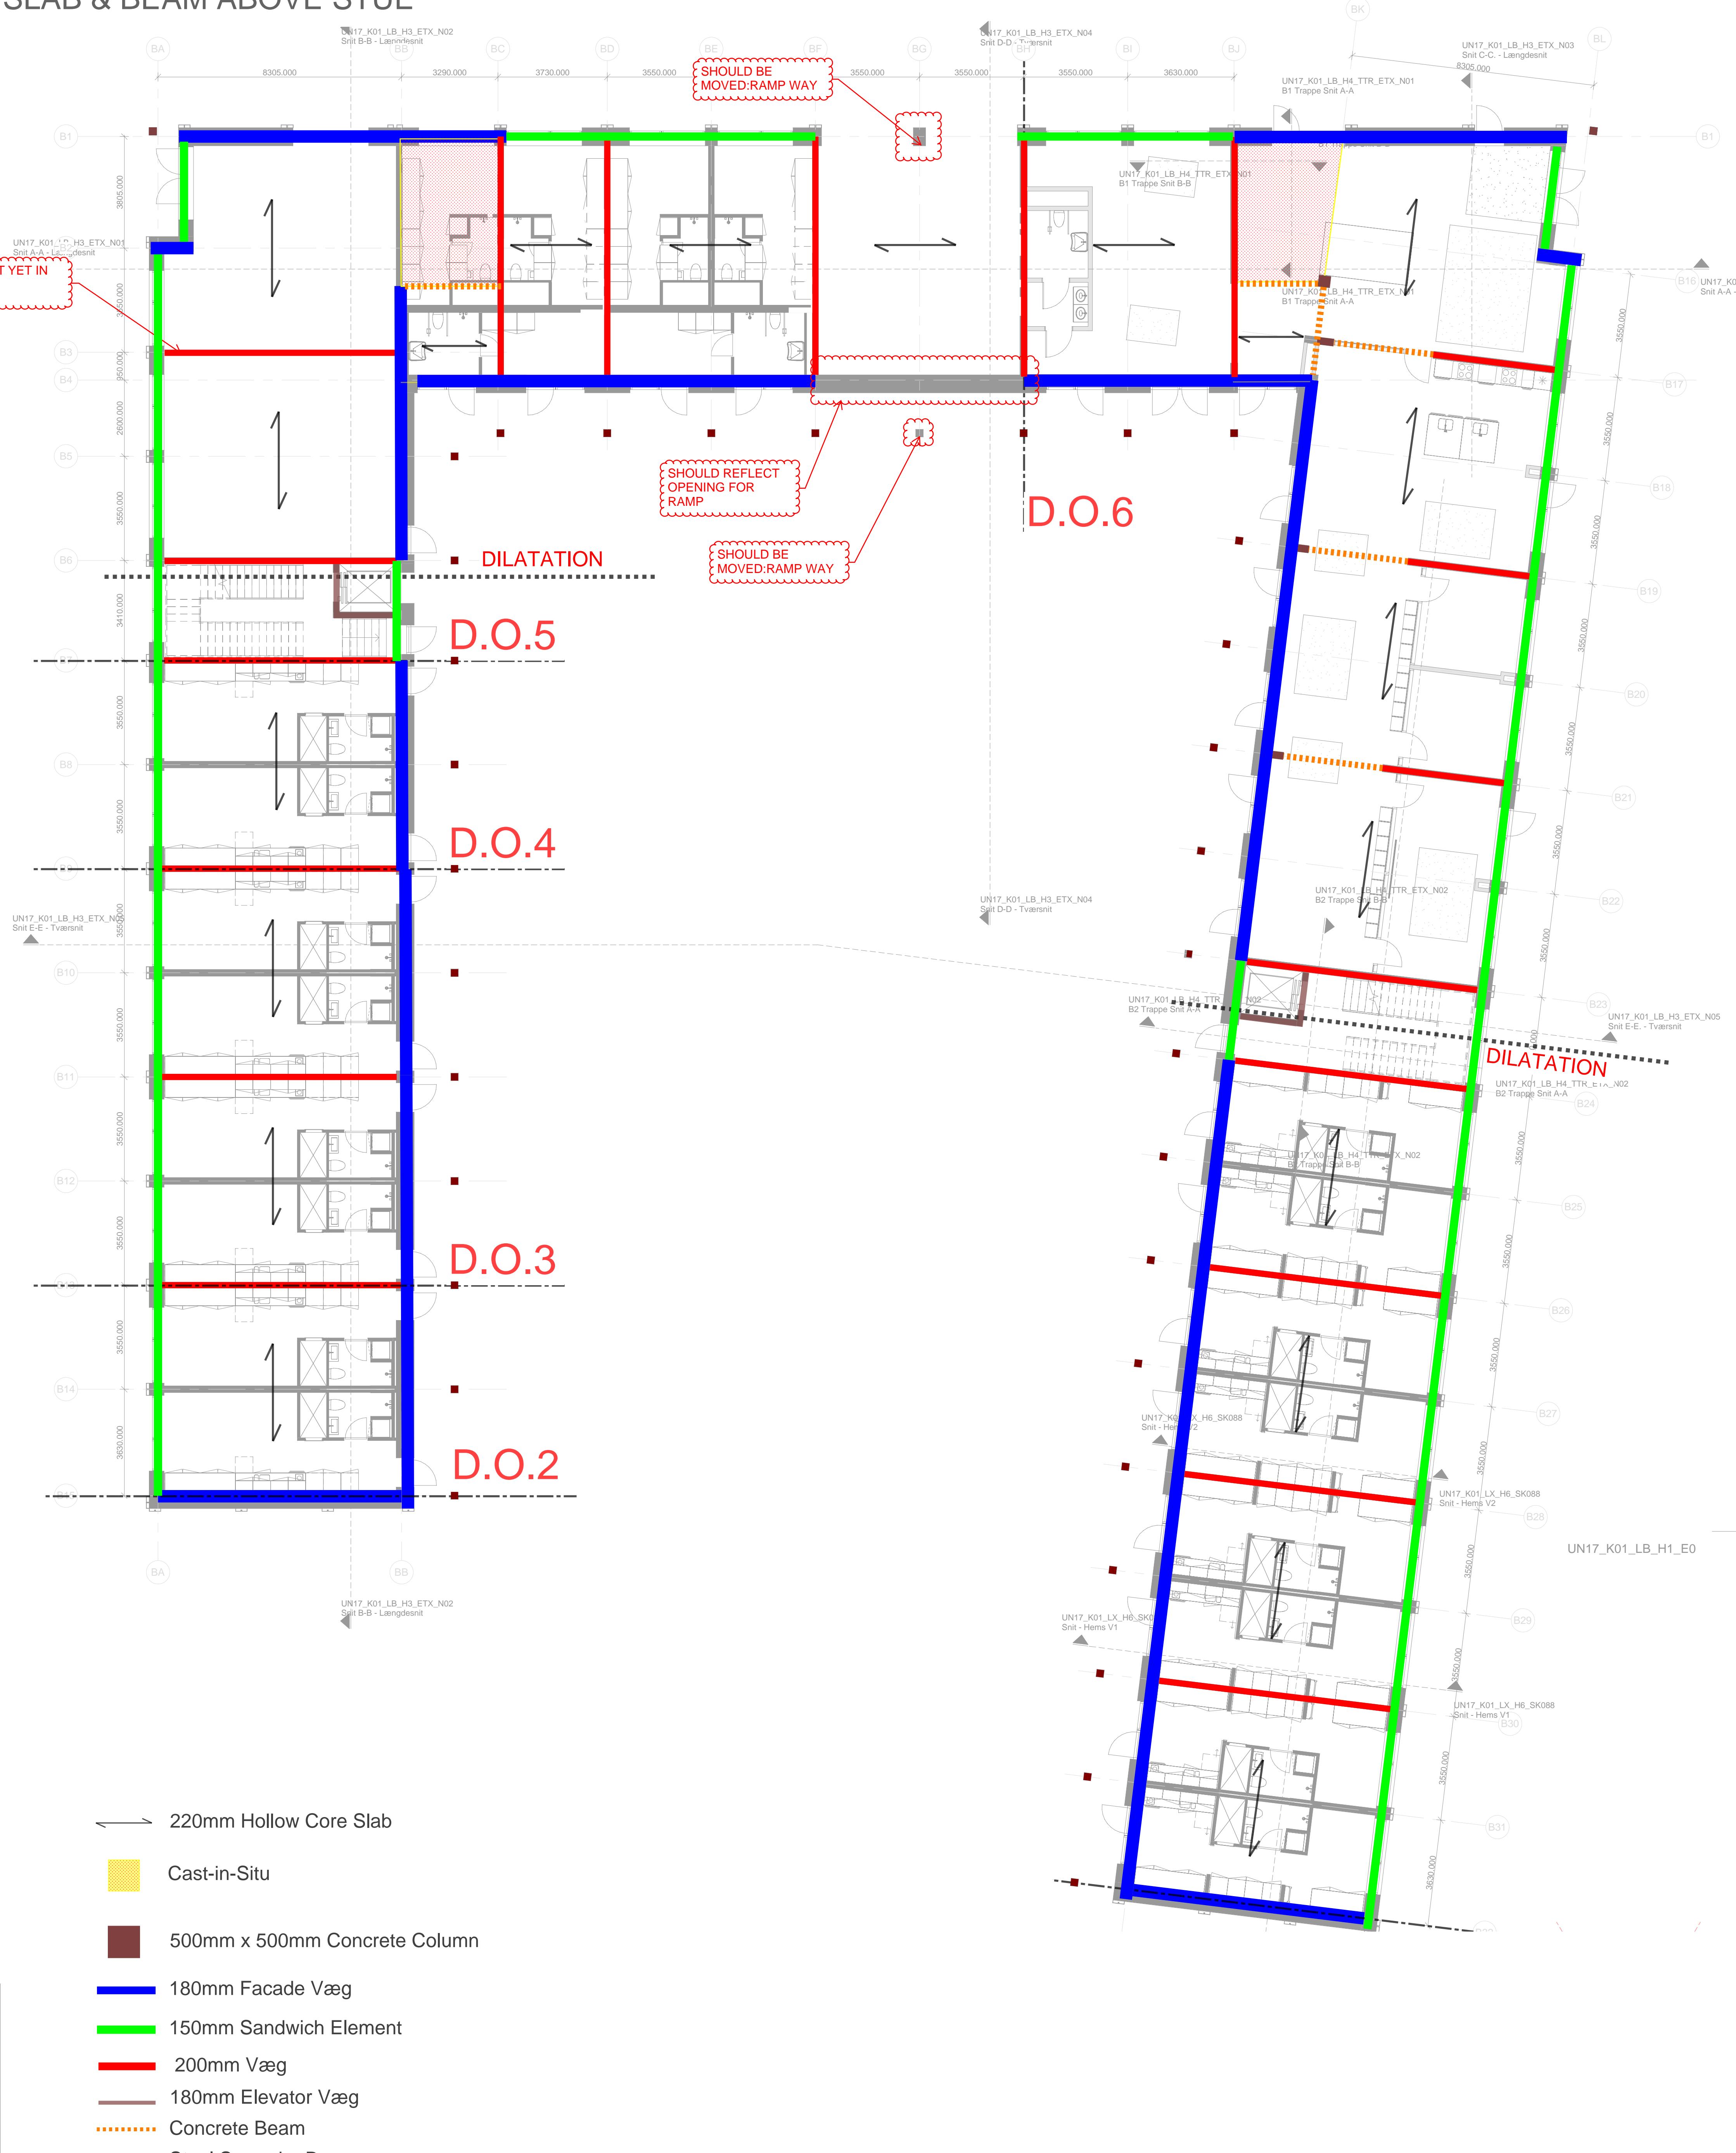

WALLS & COLUMNS IN 1.sal
SLAB & BEAM ABOVE 1.sal

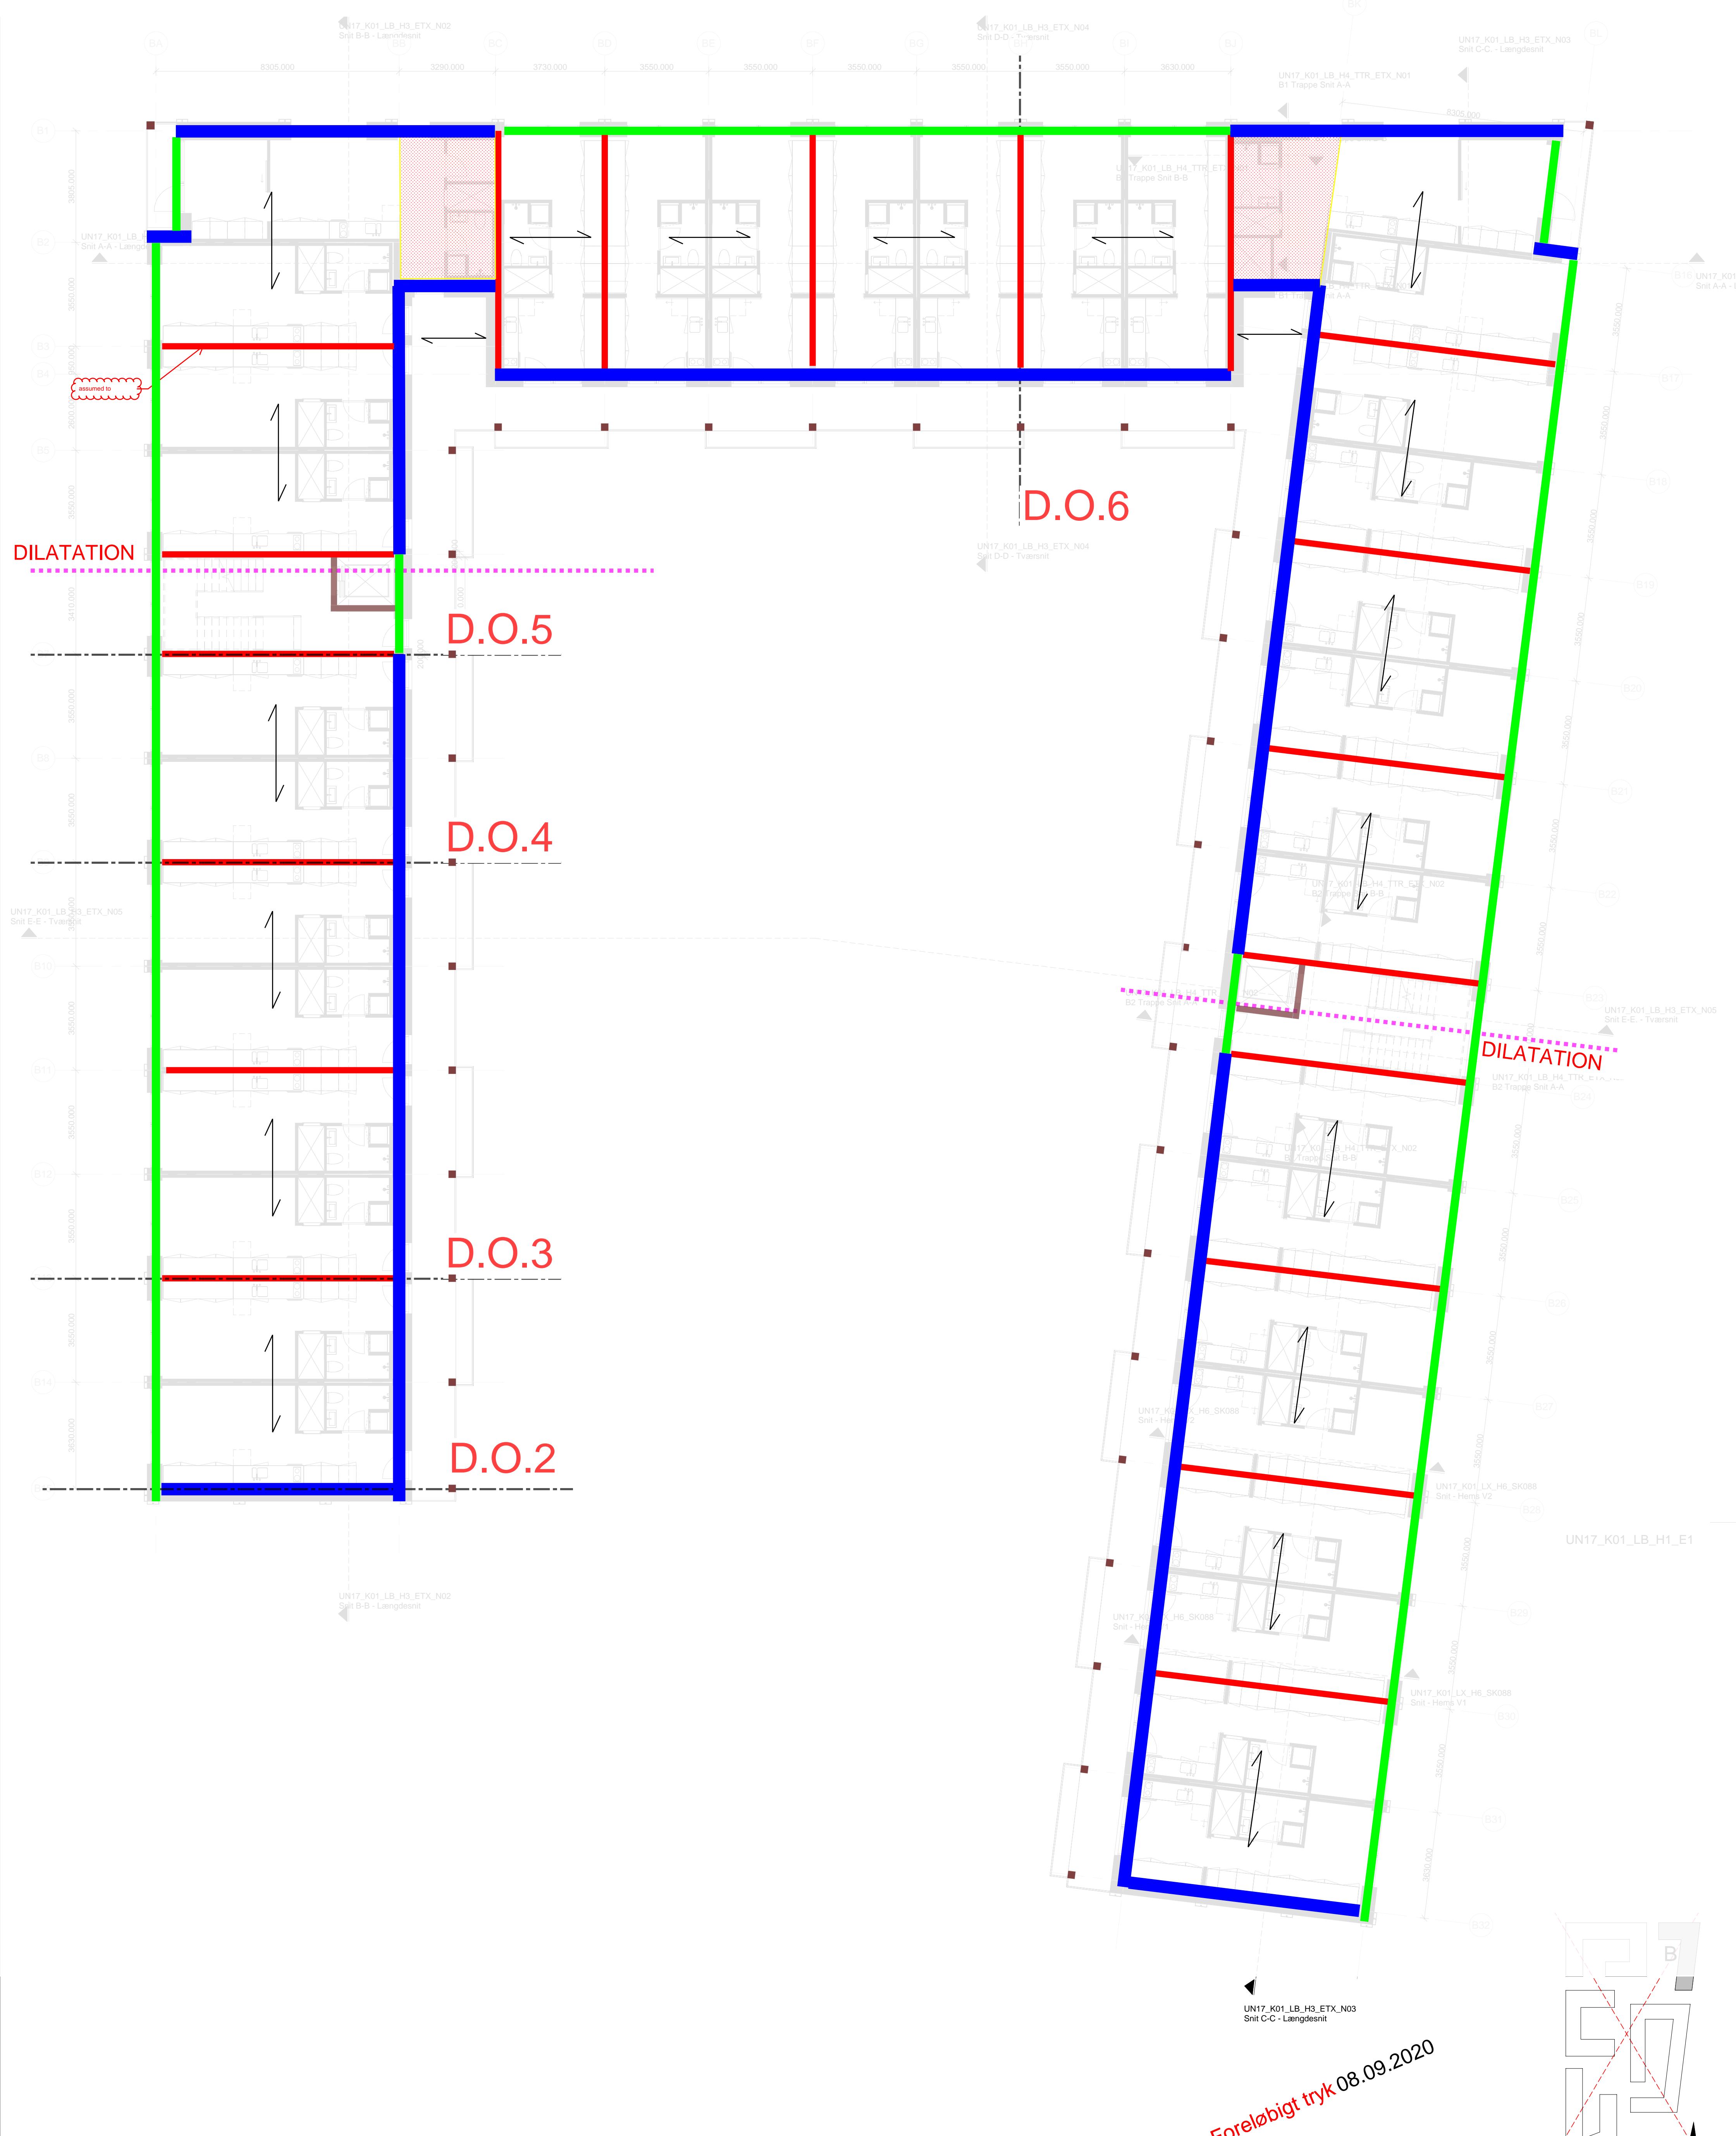

UN17 Village

Bygherre: NREP

Dato: 14.05.2020

Emne: 1. sal

Sag. nr: 118.6863

Fase: Projektfase

Mål: 1 : 100

Sign: SRM

UN17_K01_LB_H1_E1

■ Arkitekt:

ÅRSTIDERNE
ARKITEKTER

Ørestads Blvd. 41
2300 København S
T: +45 7024 2100
www.aarstiderne.dk

□ Arkitekt 2:

LENDAGER GROUP


Sundkaj 163
2150 Nordhavn
T: +45 61280090
www.lendager.com

■ Ingenier:

MOE
ARTELIA GROUP

Buddingevej 272
2680 Søborg
T: +45 44576000
www.moe.dk

WALLS & COLUMNS IN 2.sal
SLAB & BEAM ABOVE 2.sal

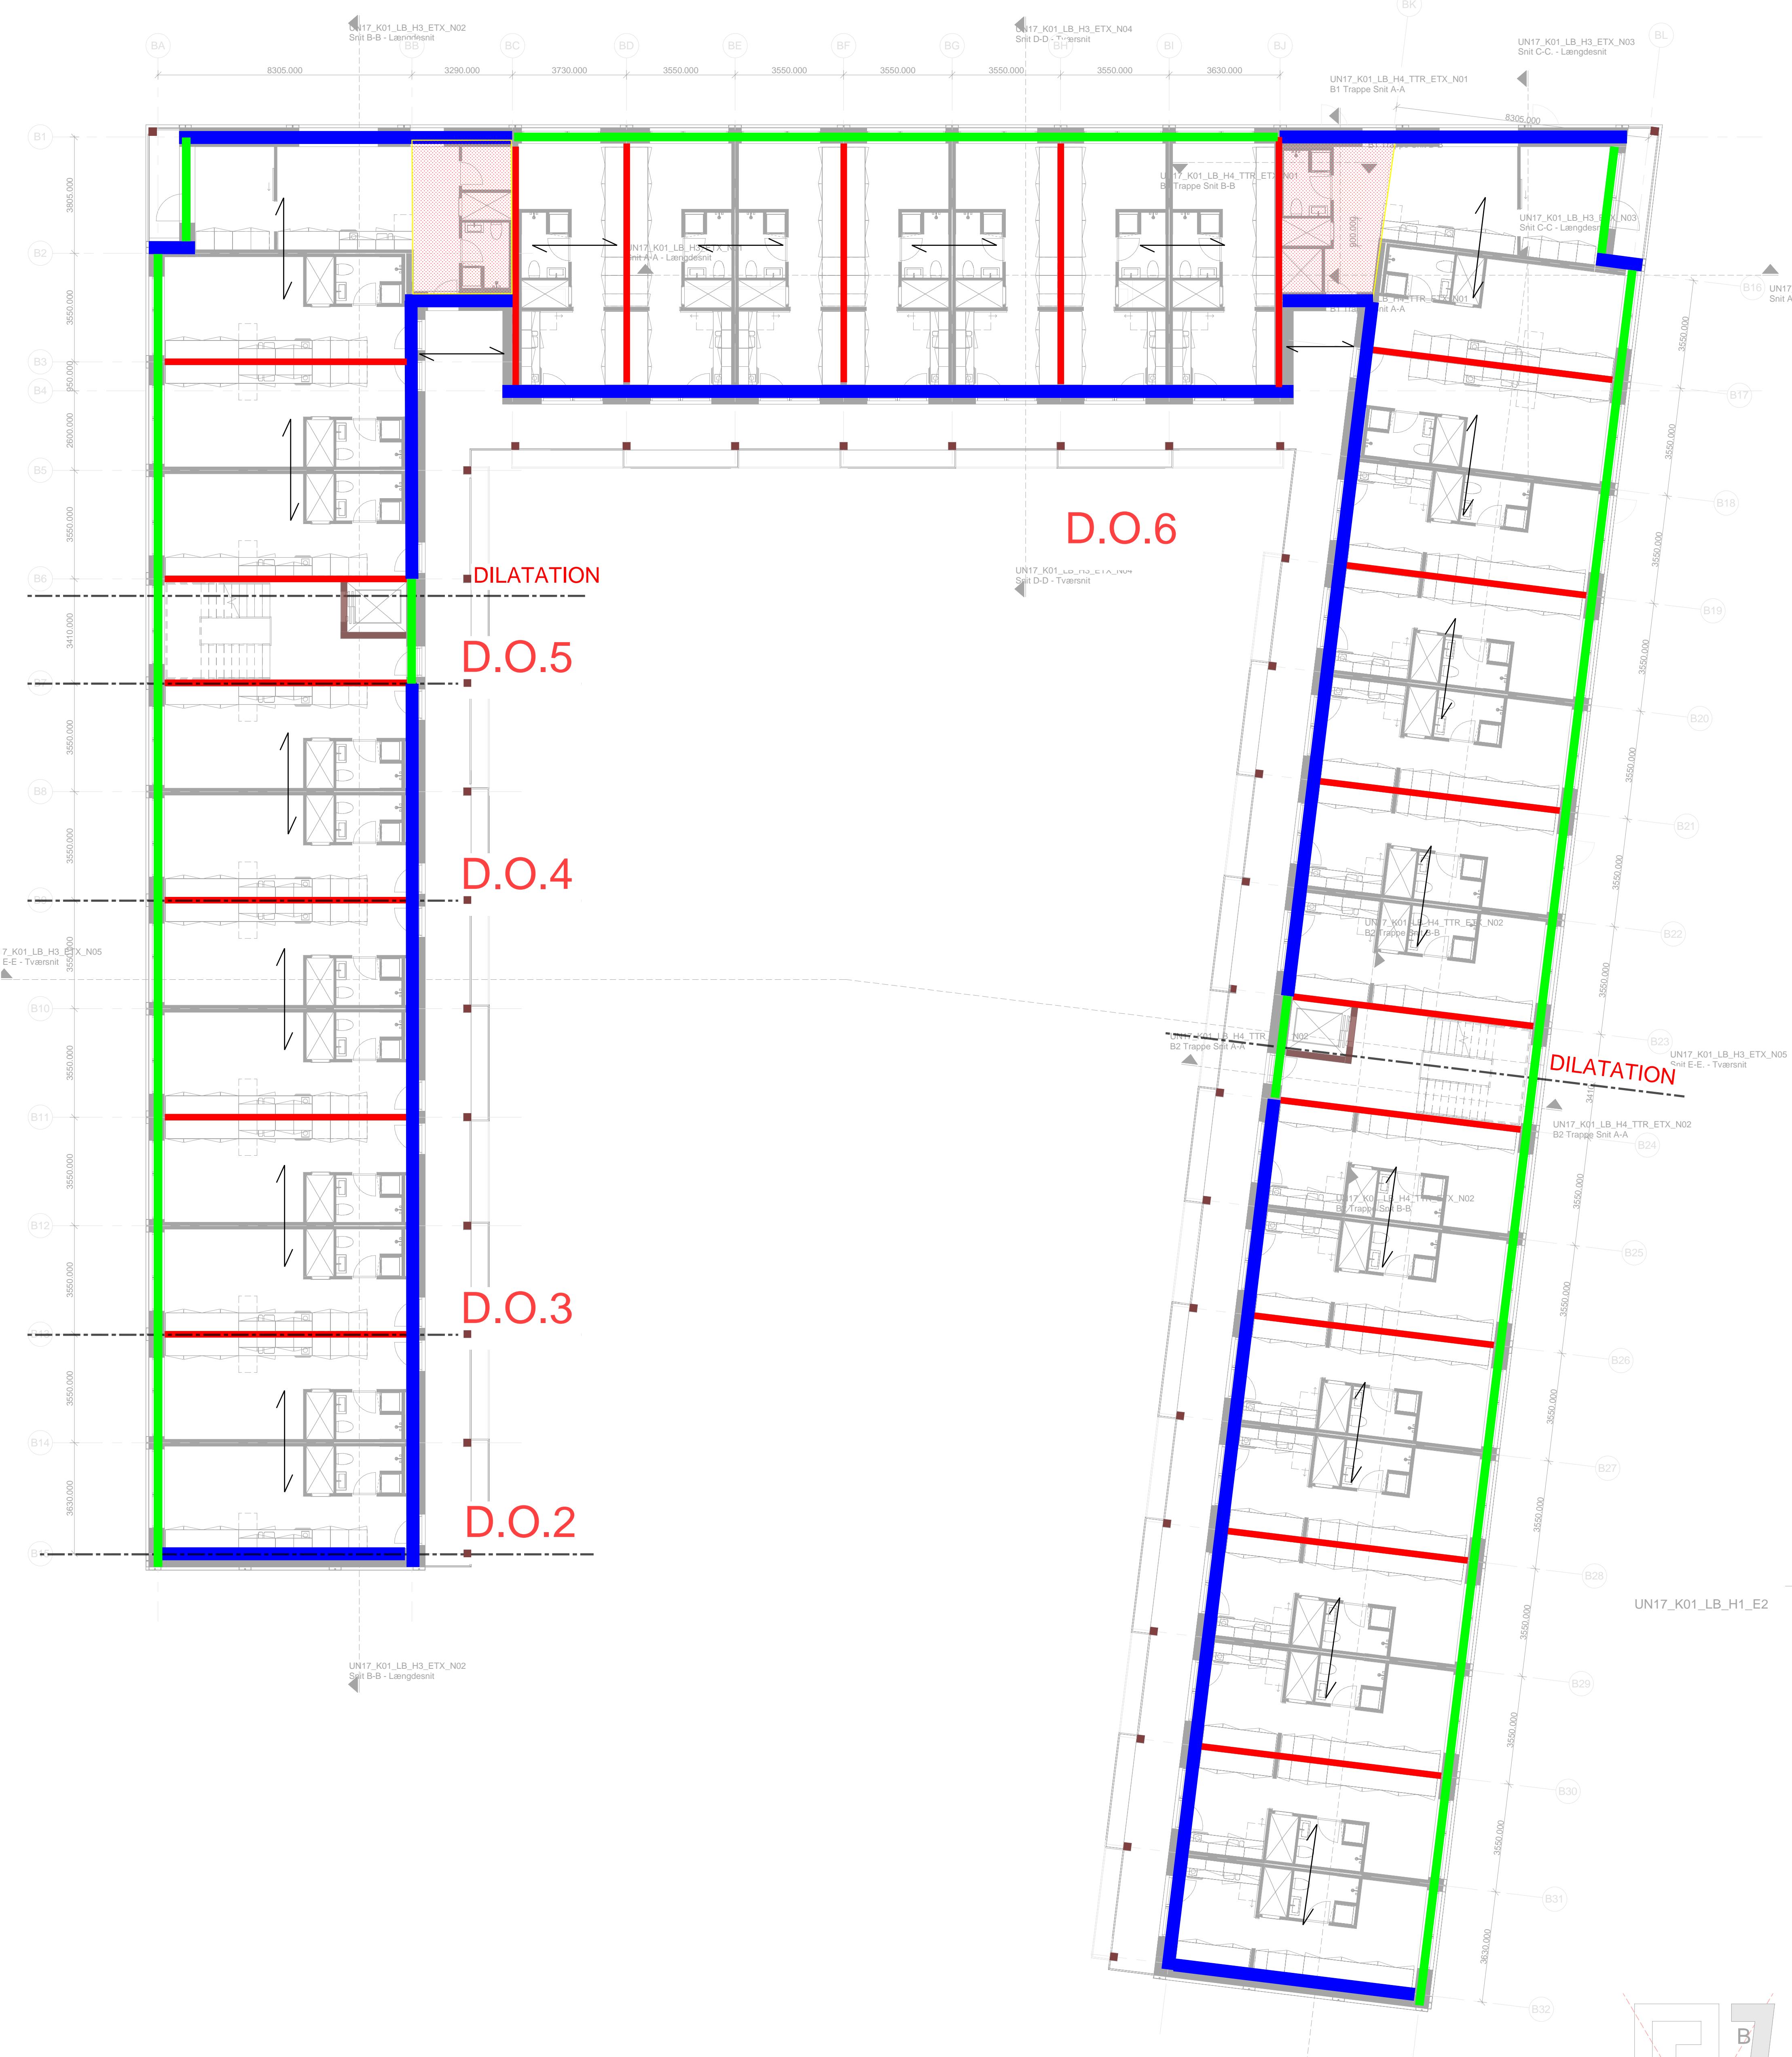

UN17 Village
Bygherre: NREP
Emne: 2. sal
Fase: Projektfase
Mål: 1 : 100
Sag. nr: 118.6863
Sign: SRM
Ørestads Blvd. 41
T: +45 7024 2100
www.aarstiderne.dk


■ Arkitekt:	ÅRSTIDERNE ARKITEKTER part of Sweco	Sundkaj 163 2150 Nordhavn	T: +45 61280090
□ Arkitekt 2:	LENDAGER GROUP	Buddingevej 272 2680 Søborg	T: +45 44576000
■ Ingenier:	MOE ARTELIA GROUP	Buddingevej 272 2680 Søborg	T: +45 44576000

Dato: 14.05.2020

www.lendager.com

www.moe.dk

WALLS & COLUMNS IN 3.sal
SLAB & BEAM ABOVE 3.sal

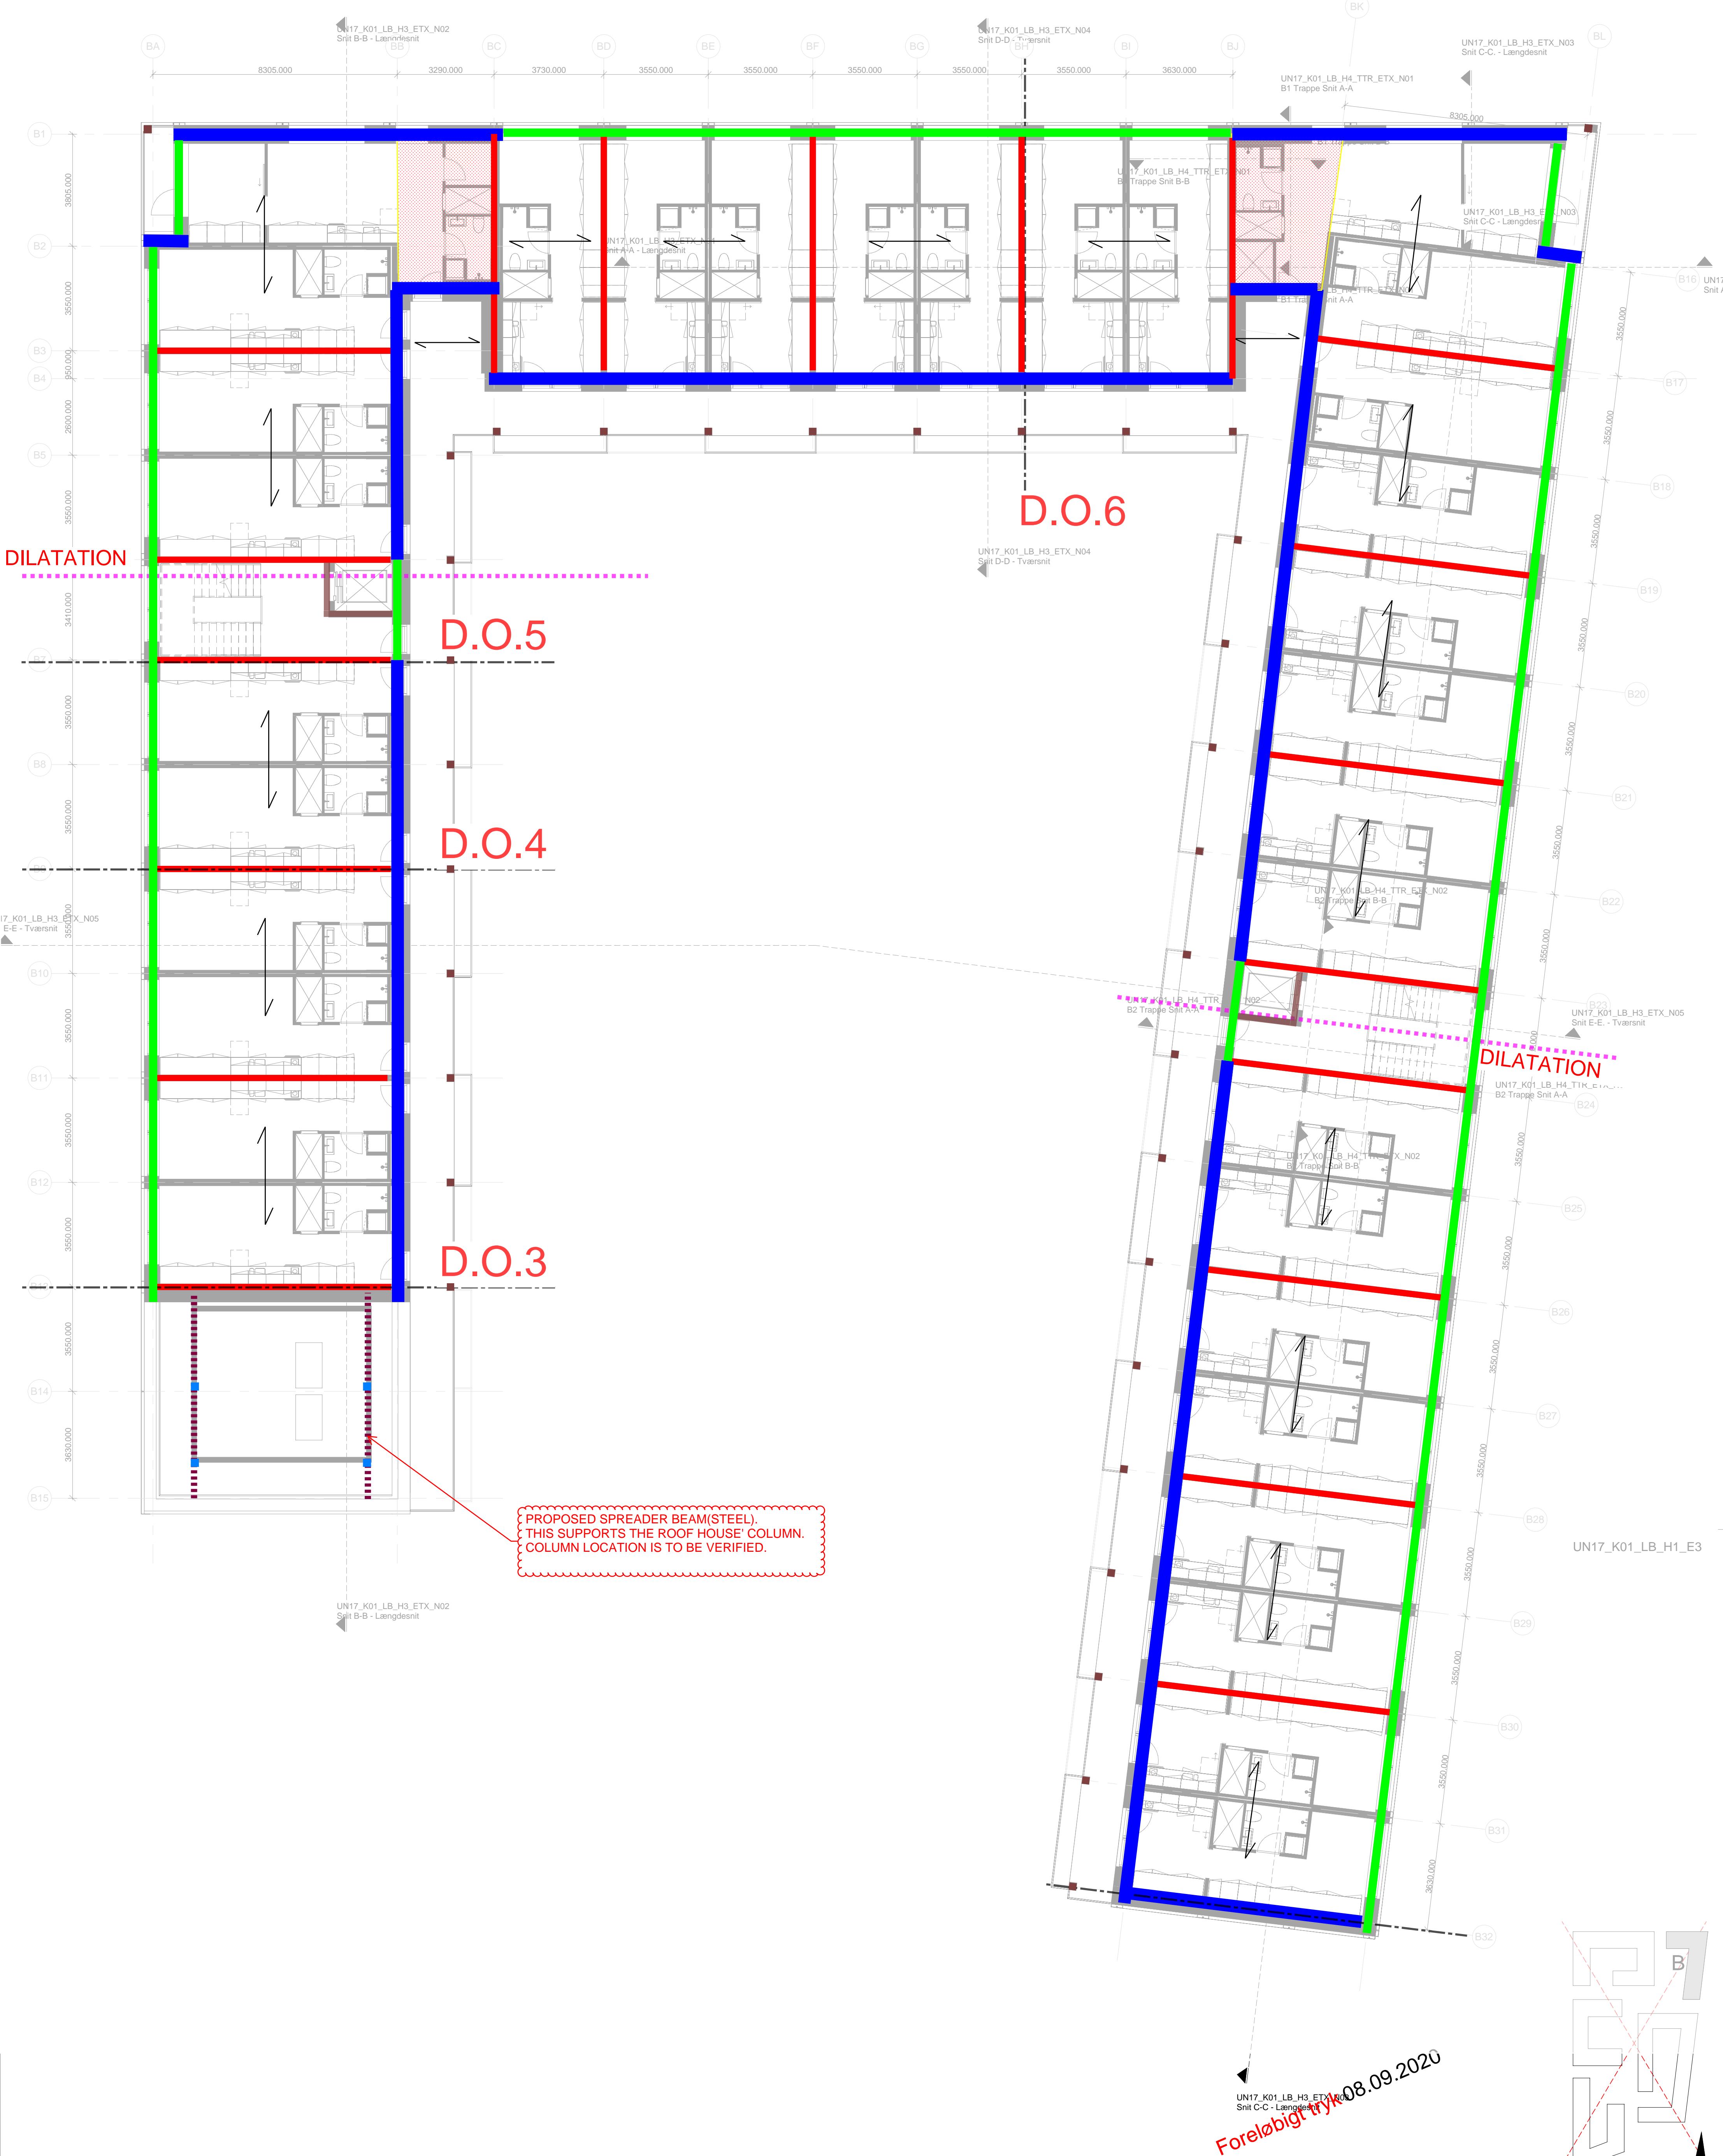

UN17 Village

Bygherre: NREP

Egne:

Fase:

Mål:

Sag. nr.:

Sign:

Ørestads Blvd. 41

T: +45 7024 2100

www.aarstiderne.dk

Projektfase

Mål: 1 : 100

SRM

2300 København S

T: +45 61280090

www.lendager.com

Arkitekt:

part of Sweco

AARSTIDERNE

ARKITEKTER

part of Sweco

Ørestads Blvd. 41

T: +45 7024 2100

www.aarstiderne.dk

Arkitekt 2:

LENDAGER GROUP

Sundkaj 163

T: +45 61280090

2150 Nordhavn

www.lendager.com

Ingenior:

MOE

Buddingevej 272


T: +45 44576000

2680 Søborg

www.moe.dk

Dato: 14.05.2020

WALLS & COLUMNS IN 4.sal
SLAB & BEAM ABOVE 4.sal

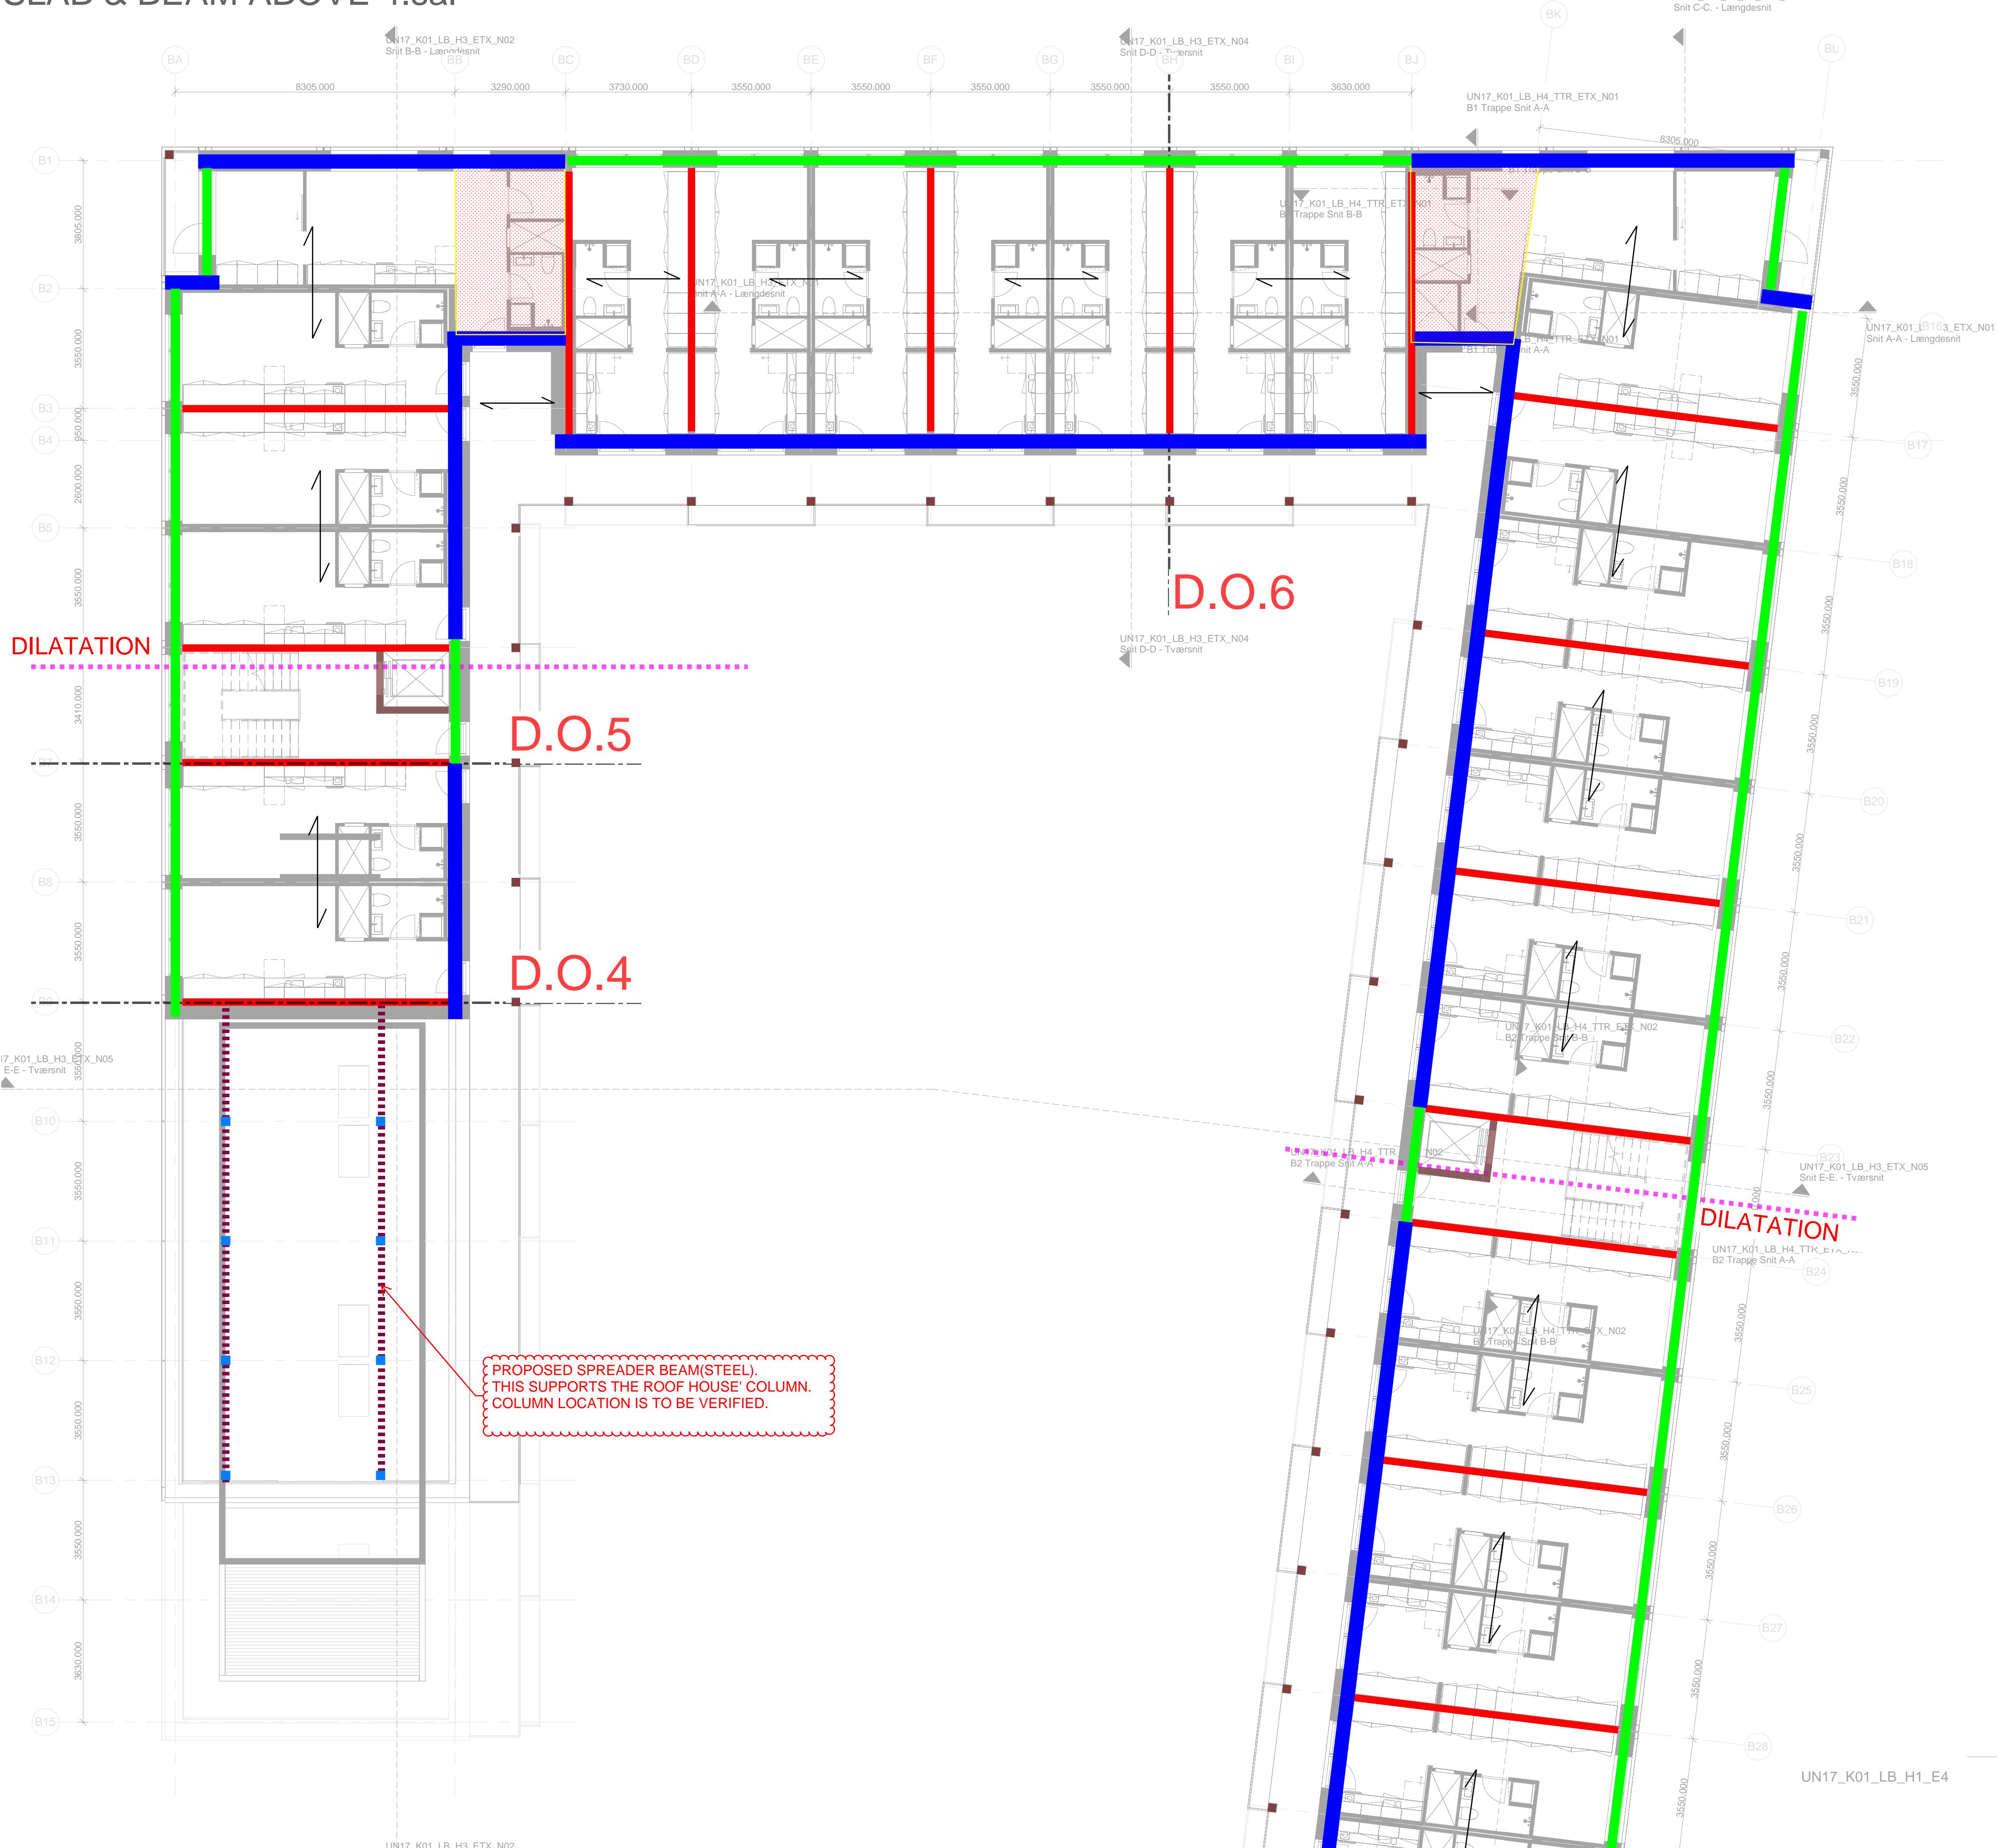

Foreløbig tryk 08.09.2020

UN17 Village

Bygherre: NREP

Ene: 4. sal

Fase: Projektfase

Mål: 1 : 100

Sag. nr: 118.6863

Sign: SRM

UN17_K01_LB_H1_E4

Dato: 14.05.2020

■ Arkitekt:

ÅRSTIDERNE
ARKITEKTER

part of Sweco

Ørestads Blvd. 41

2300 København S

T: +45 7024 2100

www.aarstiderne.dk

□ Arkitekt 2:

LENDAGER GROUP

Sundkaj 163

2150 Nordhavn

T: +45 61280090

www.lendager.com

■ Ingenier:

MOE

ARTELIA GROUP


Buddingevej 272

2680 Søborg

T: +45 44576000

www.moe.dk

WALLS & COLUMNS IN 5.sal
SLAB & BEAM ABOVE 5.sal

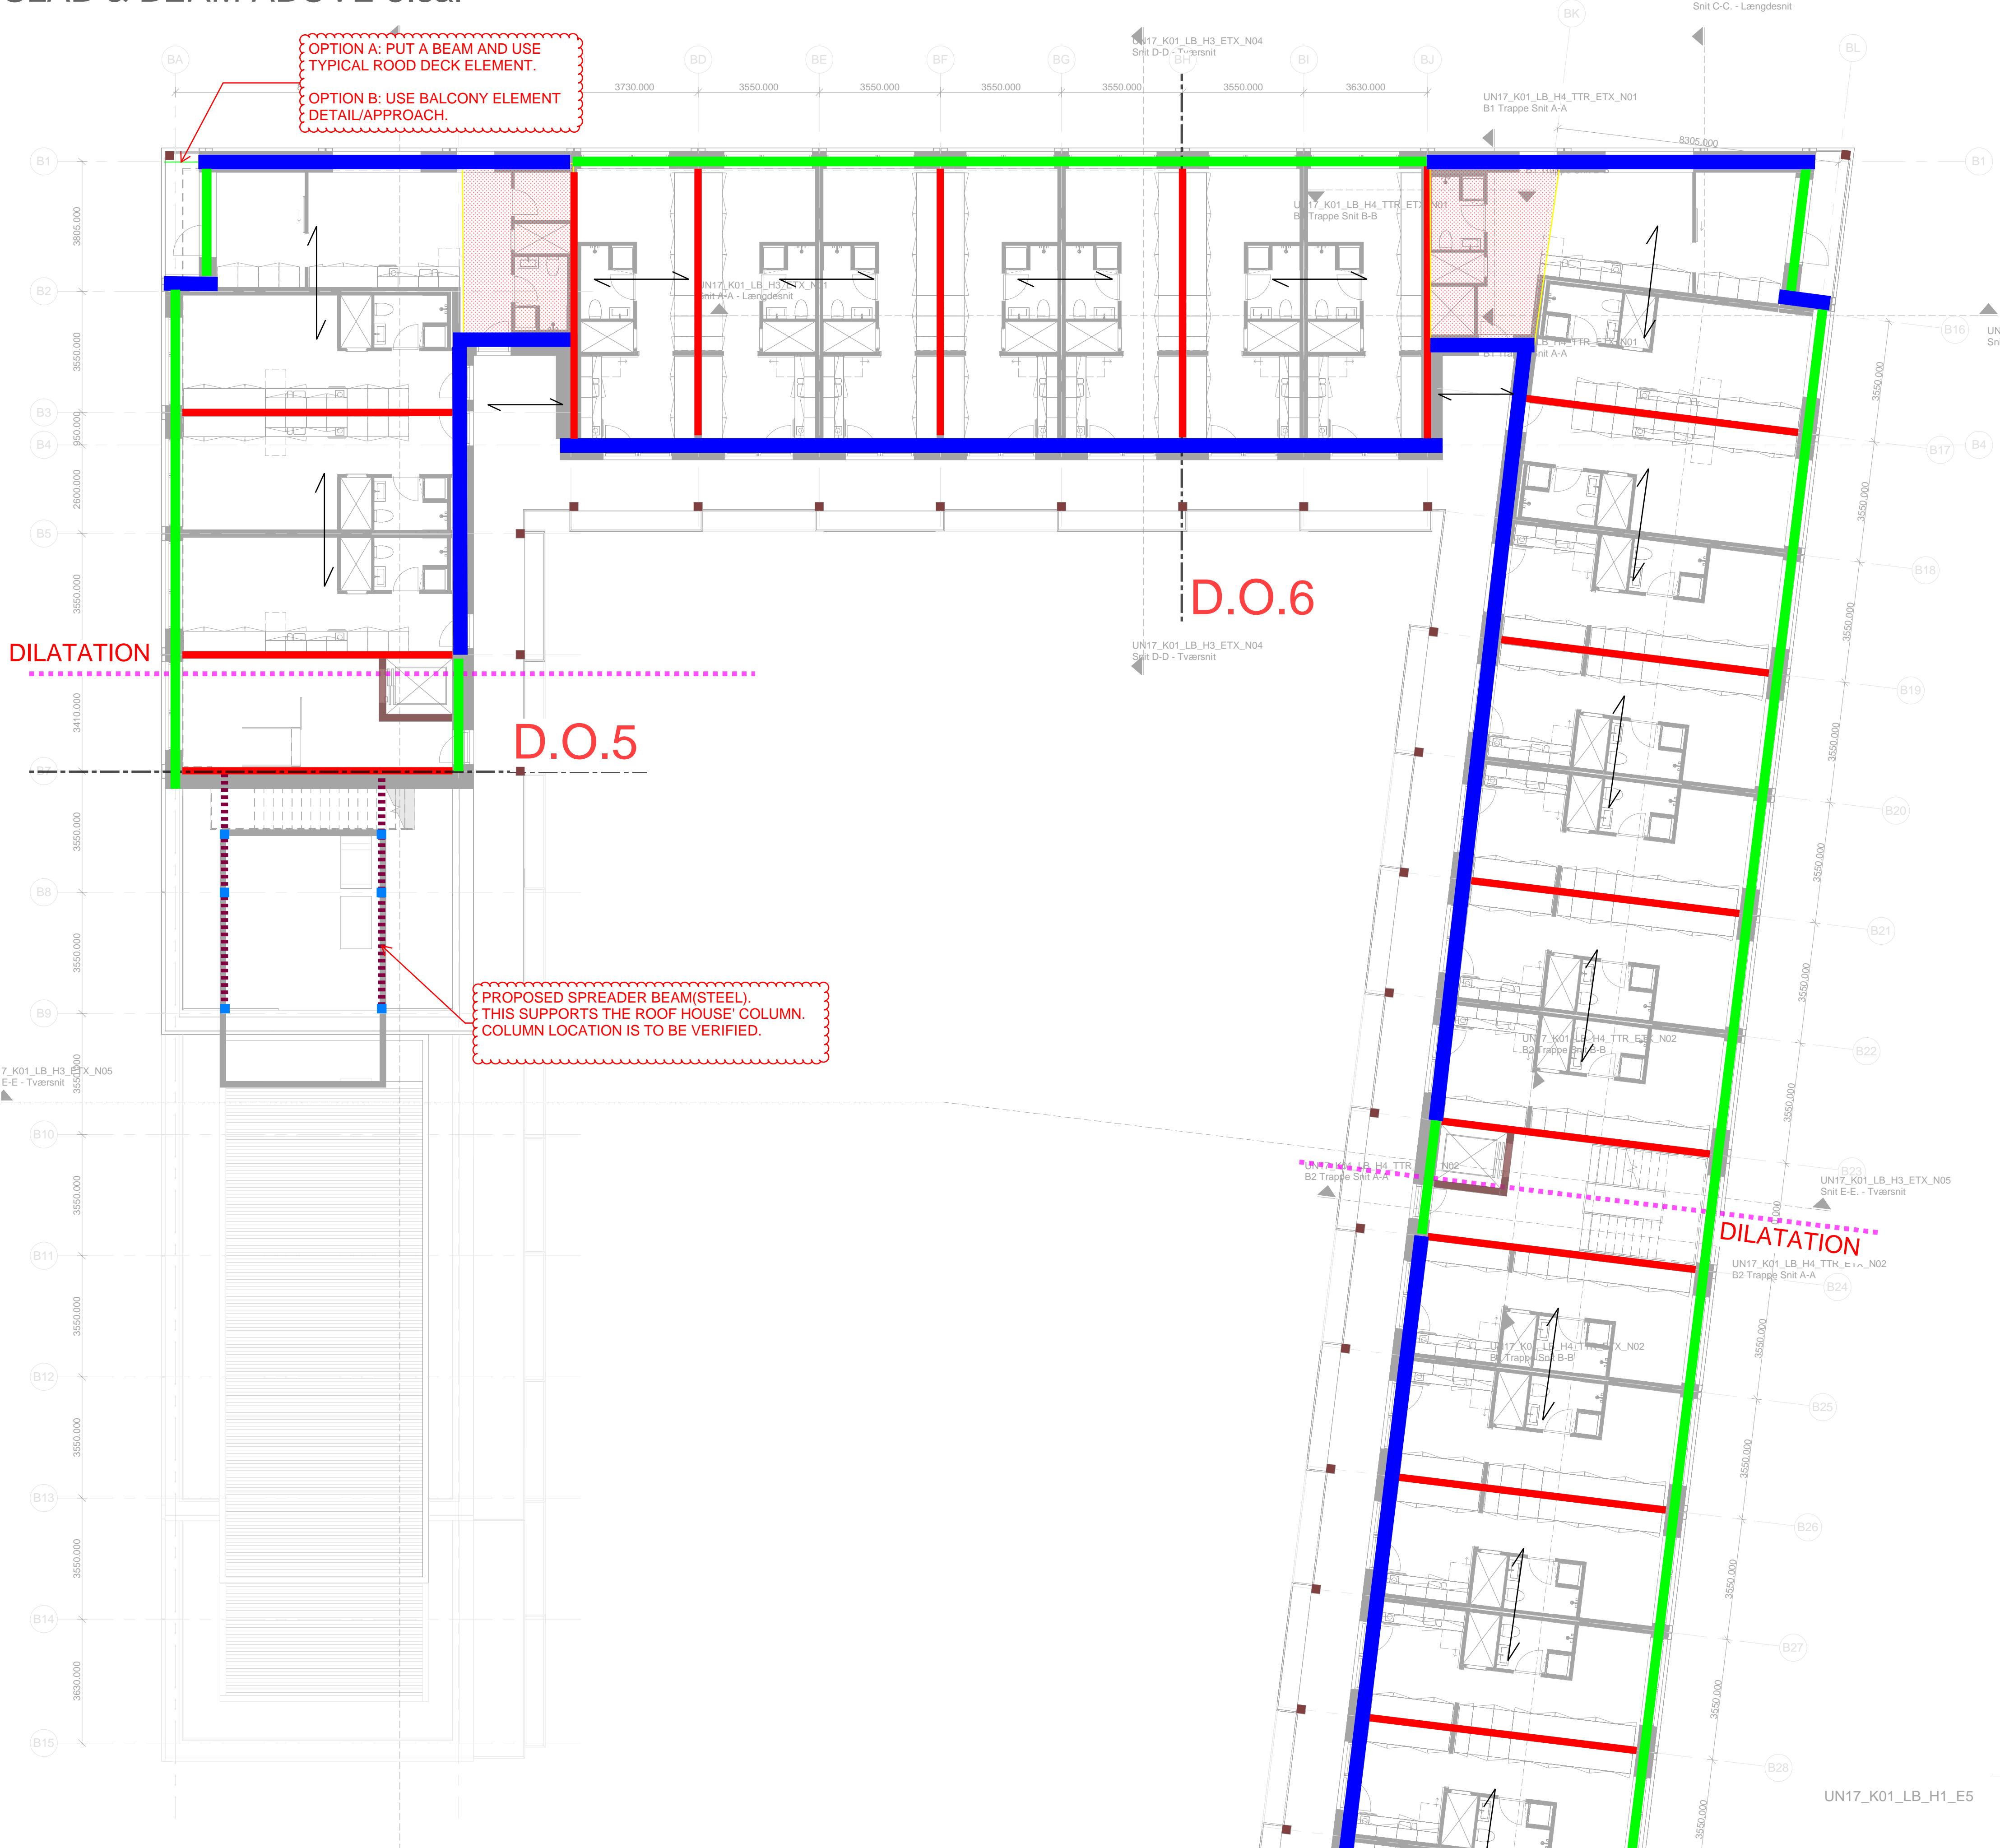

Foreløbig tryk 08.09.2020

UN17 Village

Bygherre: NREP

Emne: 5. sal

Fase: Projektfase

Mål: 1 : 100

Sag. nr: 118.6863

Sign: SRM


UN17_K01_LB_H1_E5

Dato: 14.05.2020

<input checked="" type="checkbox"/> Arkitekt:	AARSTIDERNE ARKITEKTER part of Sweco	Ørestads Blvd. 41 2300 København S	T: +45 7024 2100	www.aarstiderne.dk
<input type="checkbox"/> Arkitekt 2:	LENDAGER GROUP	Sundkaj 163 2150 Nordhavn	T: +45 61280090	www.lendager.com
<input type="checkbox"/> Ingeniør:	MOE ARTELIA GROUP	Buddingevej 272 2680 Søborg	T: +45 44576000	www.moe.dk

WALLS & COLUMNS IN 6.sal

SLAB & BEAM ABOVE 6.sal

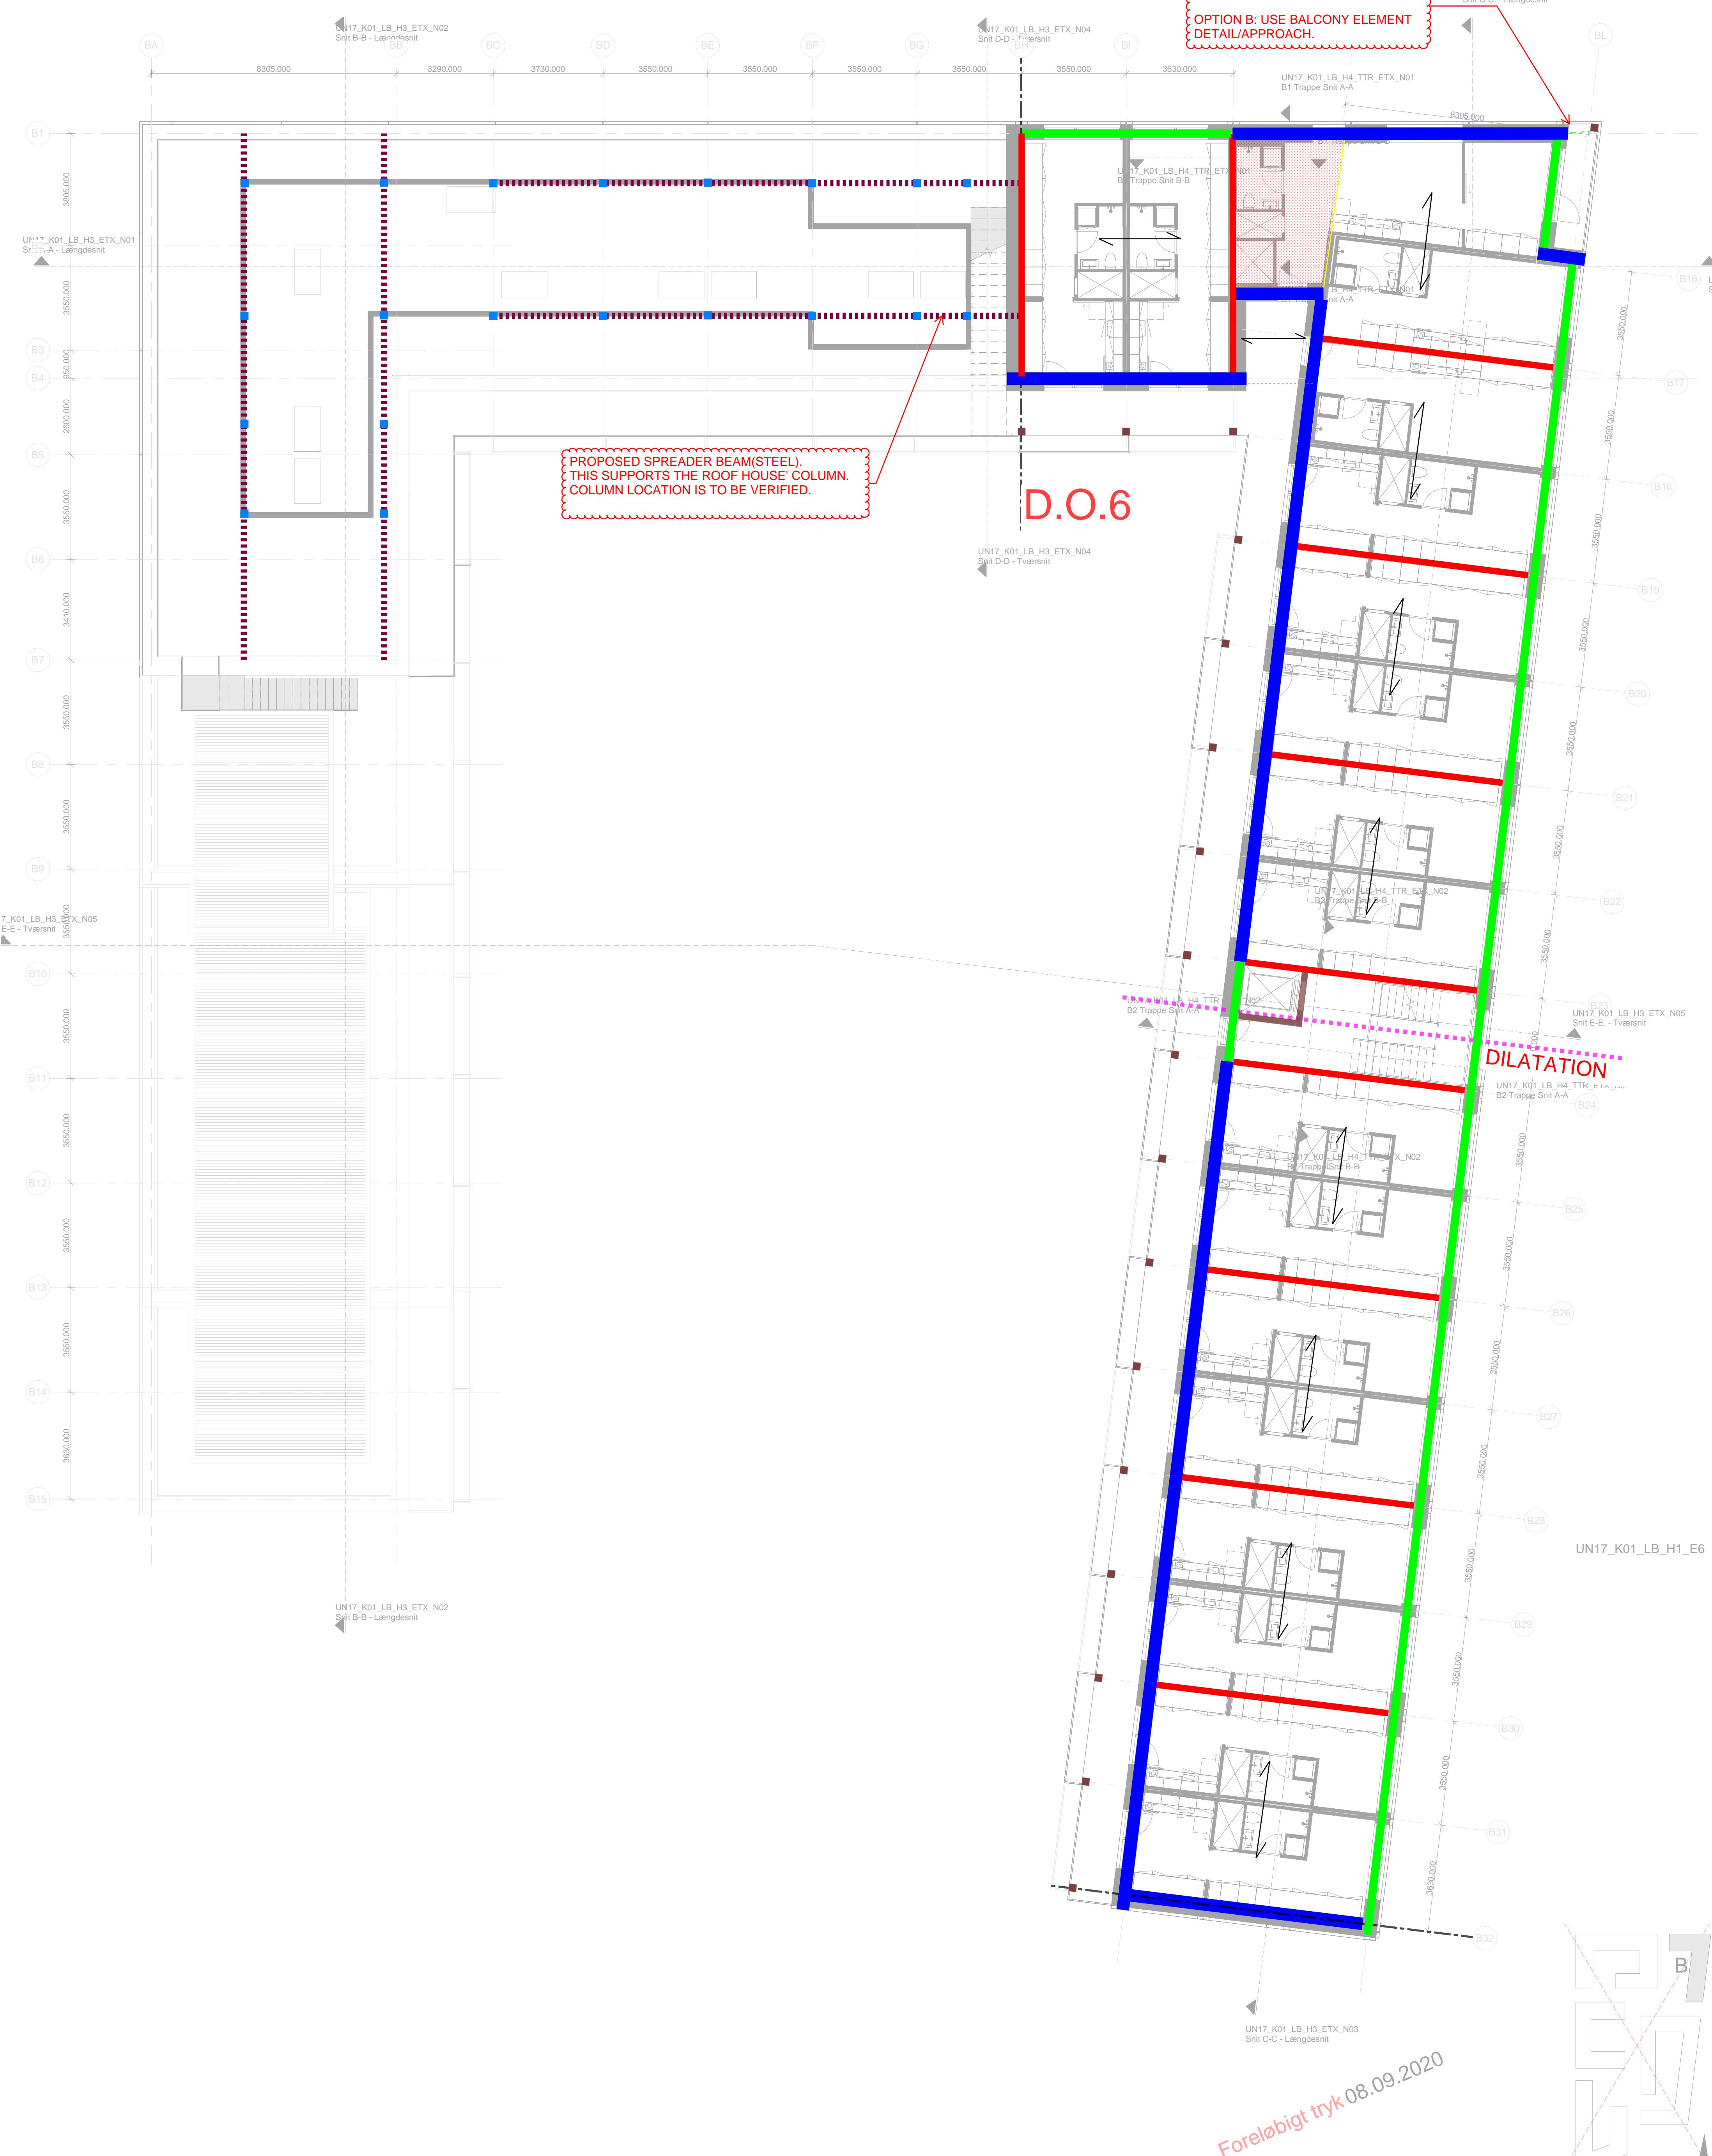

UN17 Village

Bygherre: NREP

Emne: 6. sal

Fase: Projektfase

Mål: 1 : 100

Sag. nr: 118.6863

Sign: SRM

Date: 14.05.2020

Ørestads Blvd. 41

T: +45 7024 2100

2300 København S

www.aarstiderne.dk

■ Arkitekt:

ÅRSTIDERNE
ARKITEKTER

part of Sweco

Sundkaj 163

T: +45 61280090

2150 Nordhavn

www.lendager.com

□ Arkitekt 2:

LENDAGER GROUP

Buddingevej 272

T: +45 44576000

2680 Søborg

www.moe.dk

■ Ingenier:

MOE

ARTELIA GROUP

Buddingevej 272


T: +45 44576000

2680 Søborg

www.moe.dk

WALLS & COLUMNS IN 7.sal

SLAB & BEAM ABOVE 7.sal

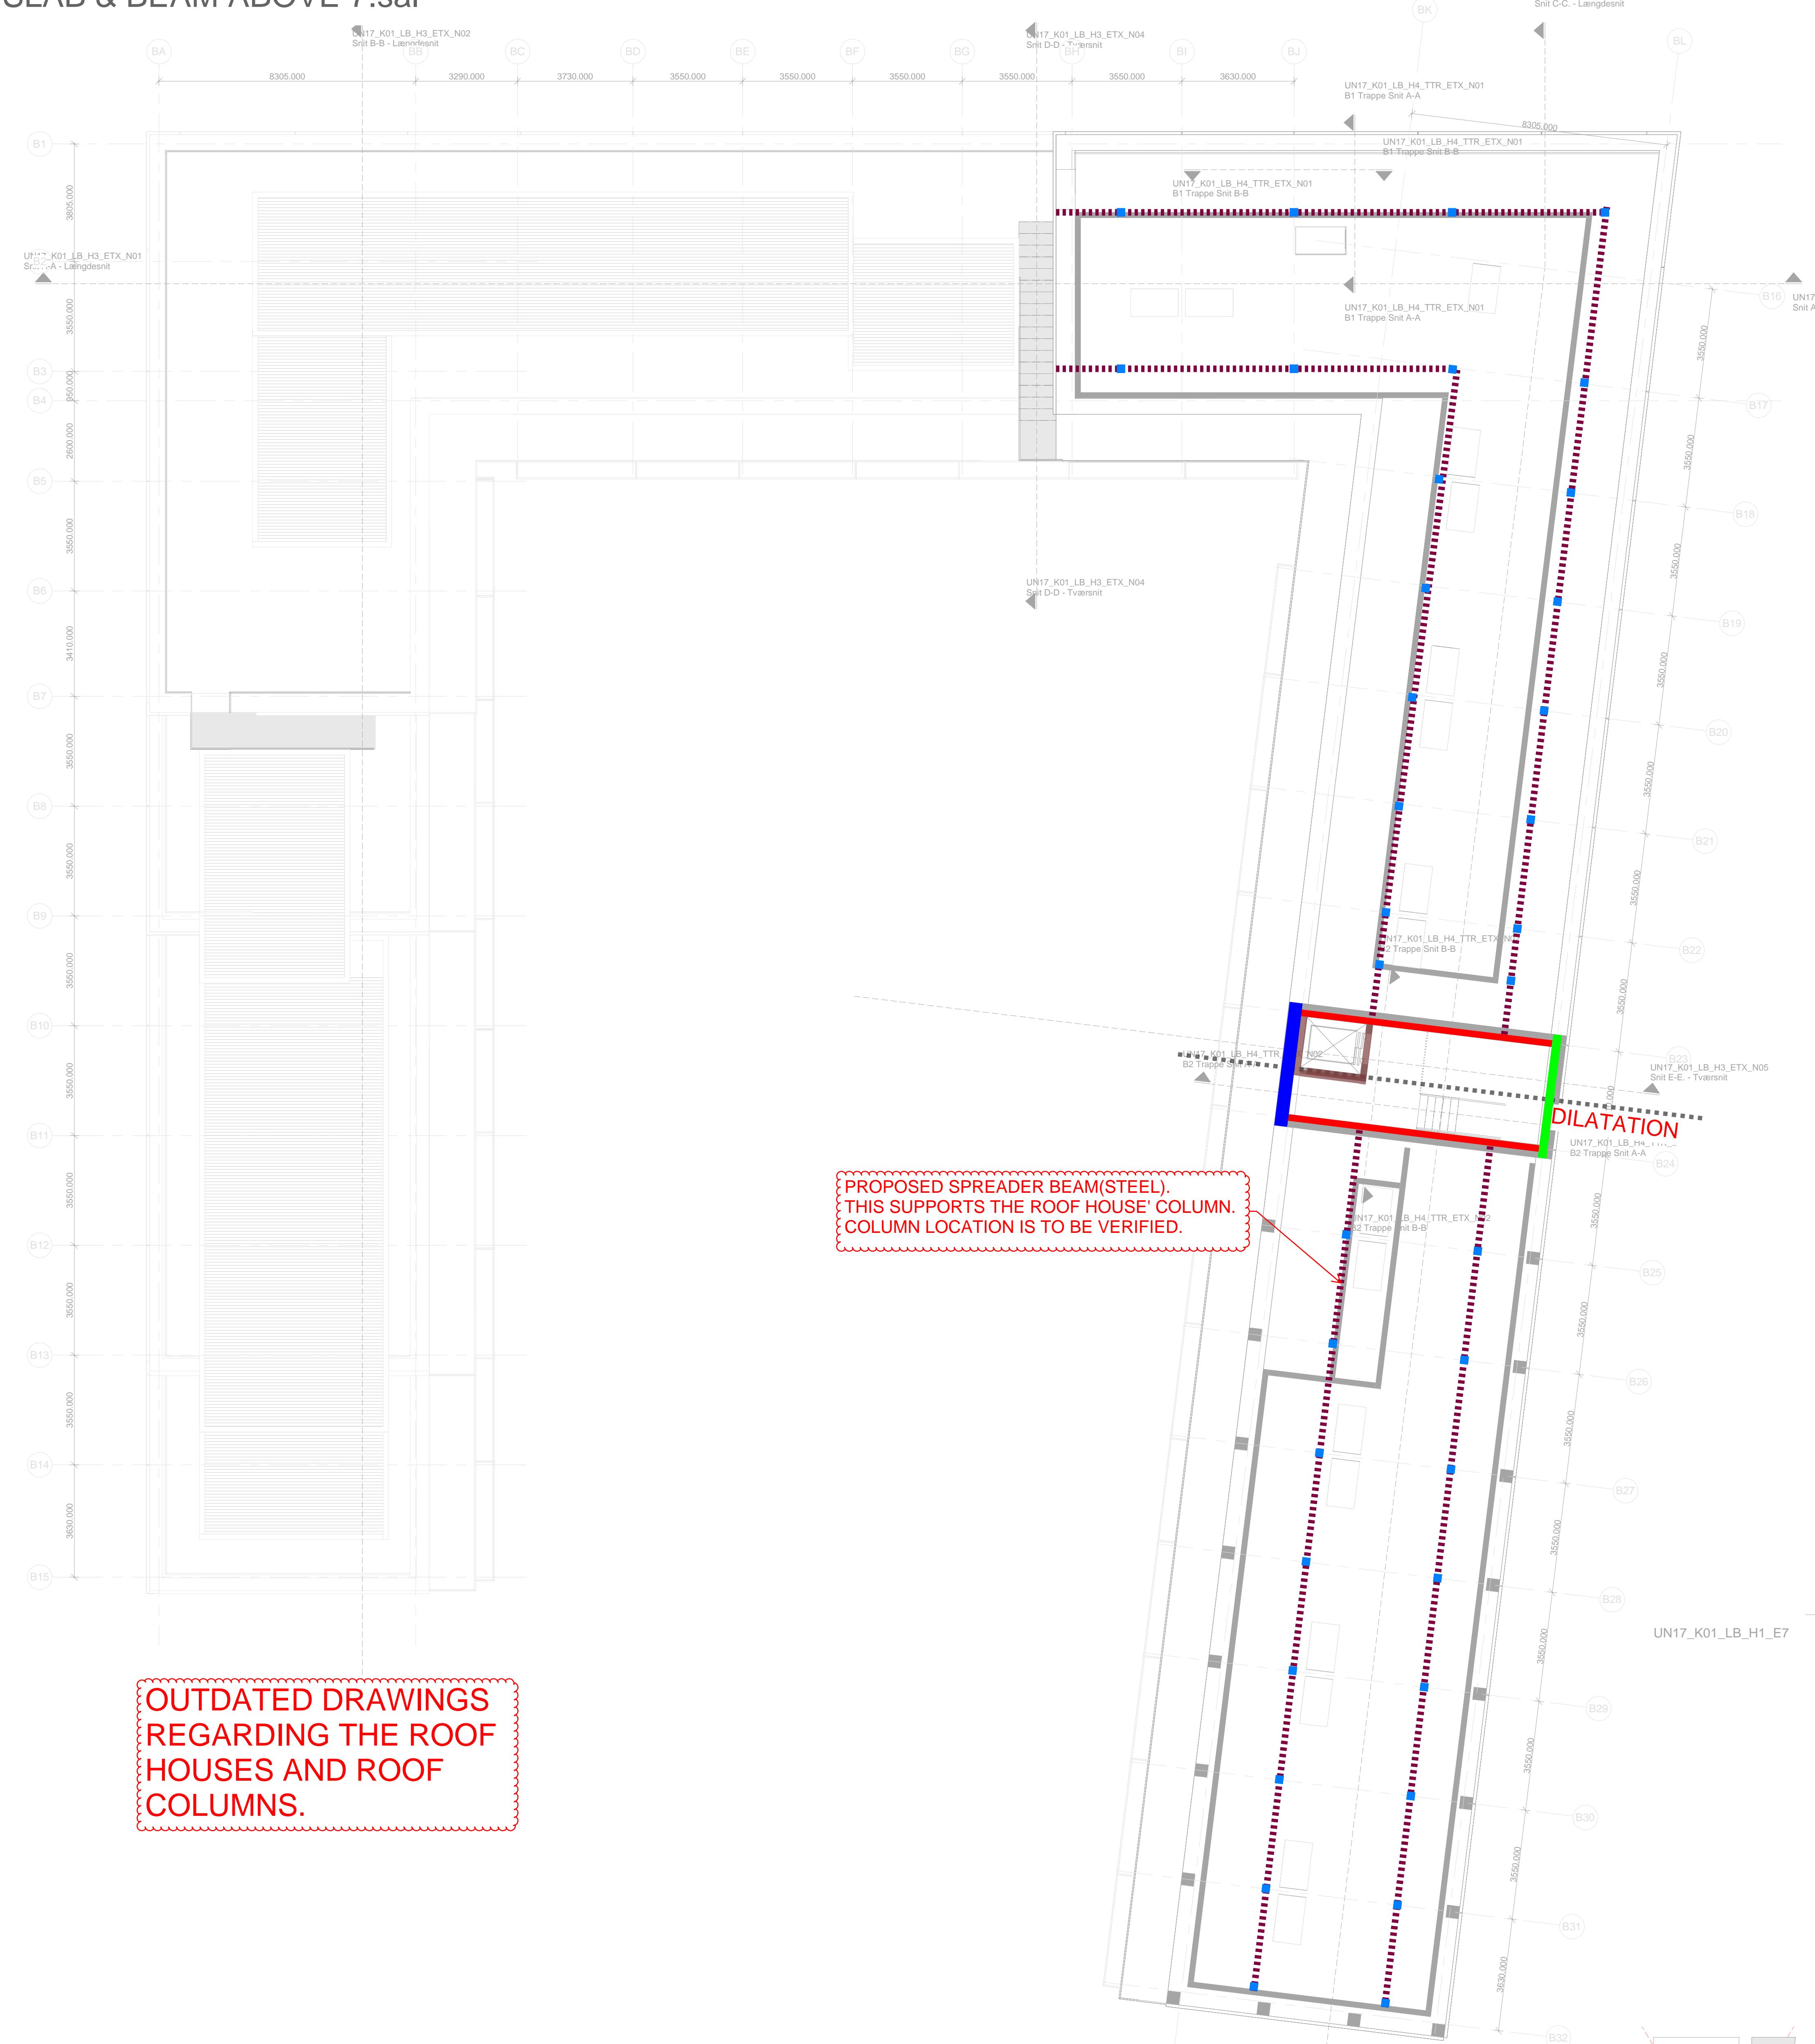

UN17 Village

Bygherre: NREP

Fase: Projektfase

Mål: 1 : 100

Sag. nr: 118.6863 Sign: SRM Date: 14.05.2020

Emne: 7. sal

Fase: Projektfase

Mål: 1 : 100

Sag. nr: 118.6863 Sign: SRM Date: 14.05.2020

■ Arkitekt:

Ørestads Blvd. 41

2300 København S

T: +45 7024 2100

www.aarstiderne.dk

■ Arkitekt 2:

Sundkaj 163

2150 Nordhavn

T: +45 61280090

www.lendager.com

■ Ingenier:

Buddingevej 272

2680 Søborg

T: +45 44576000

www.moe.dk

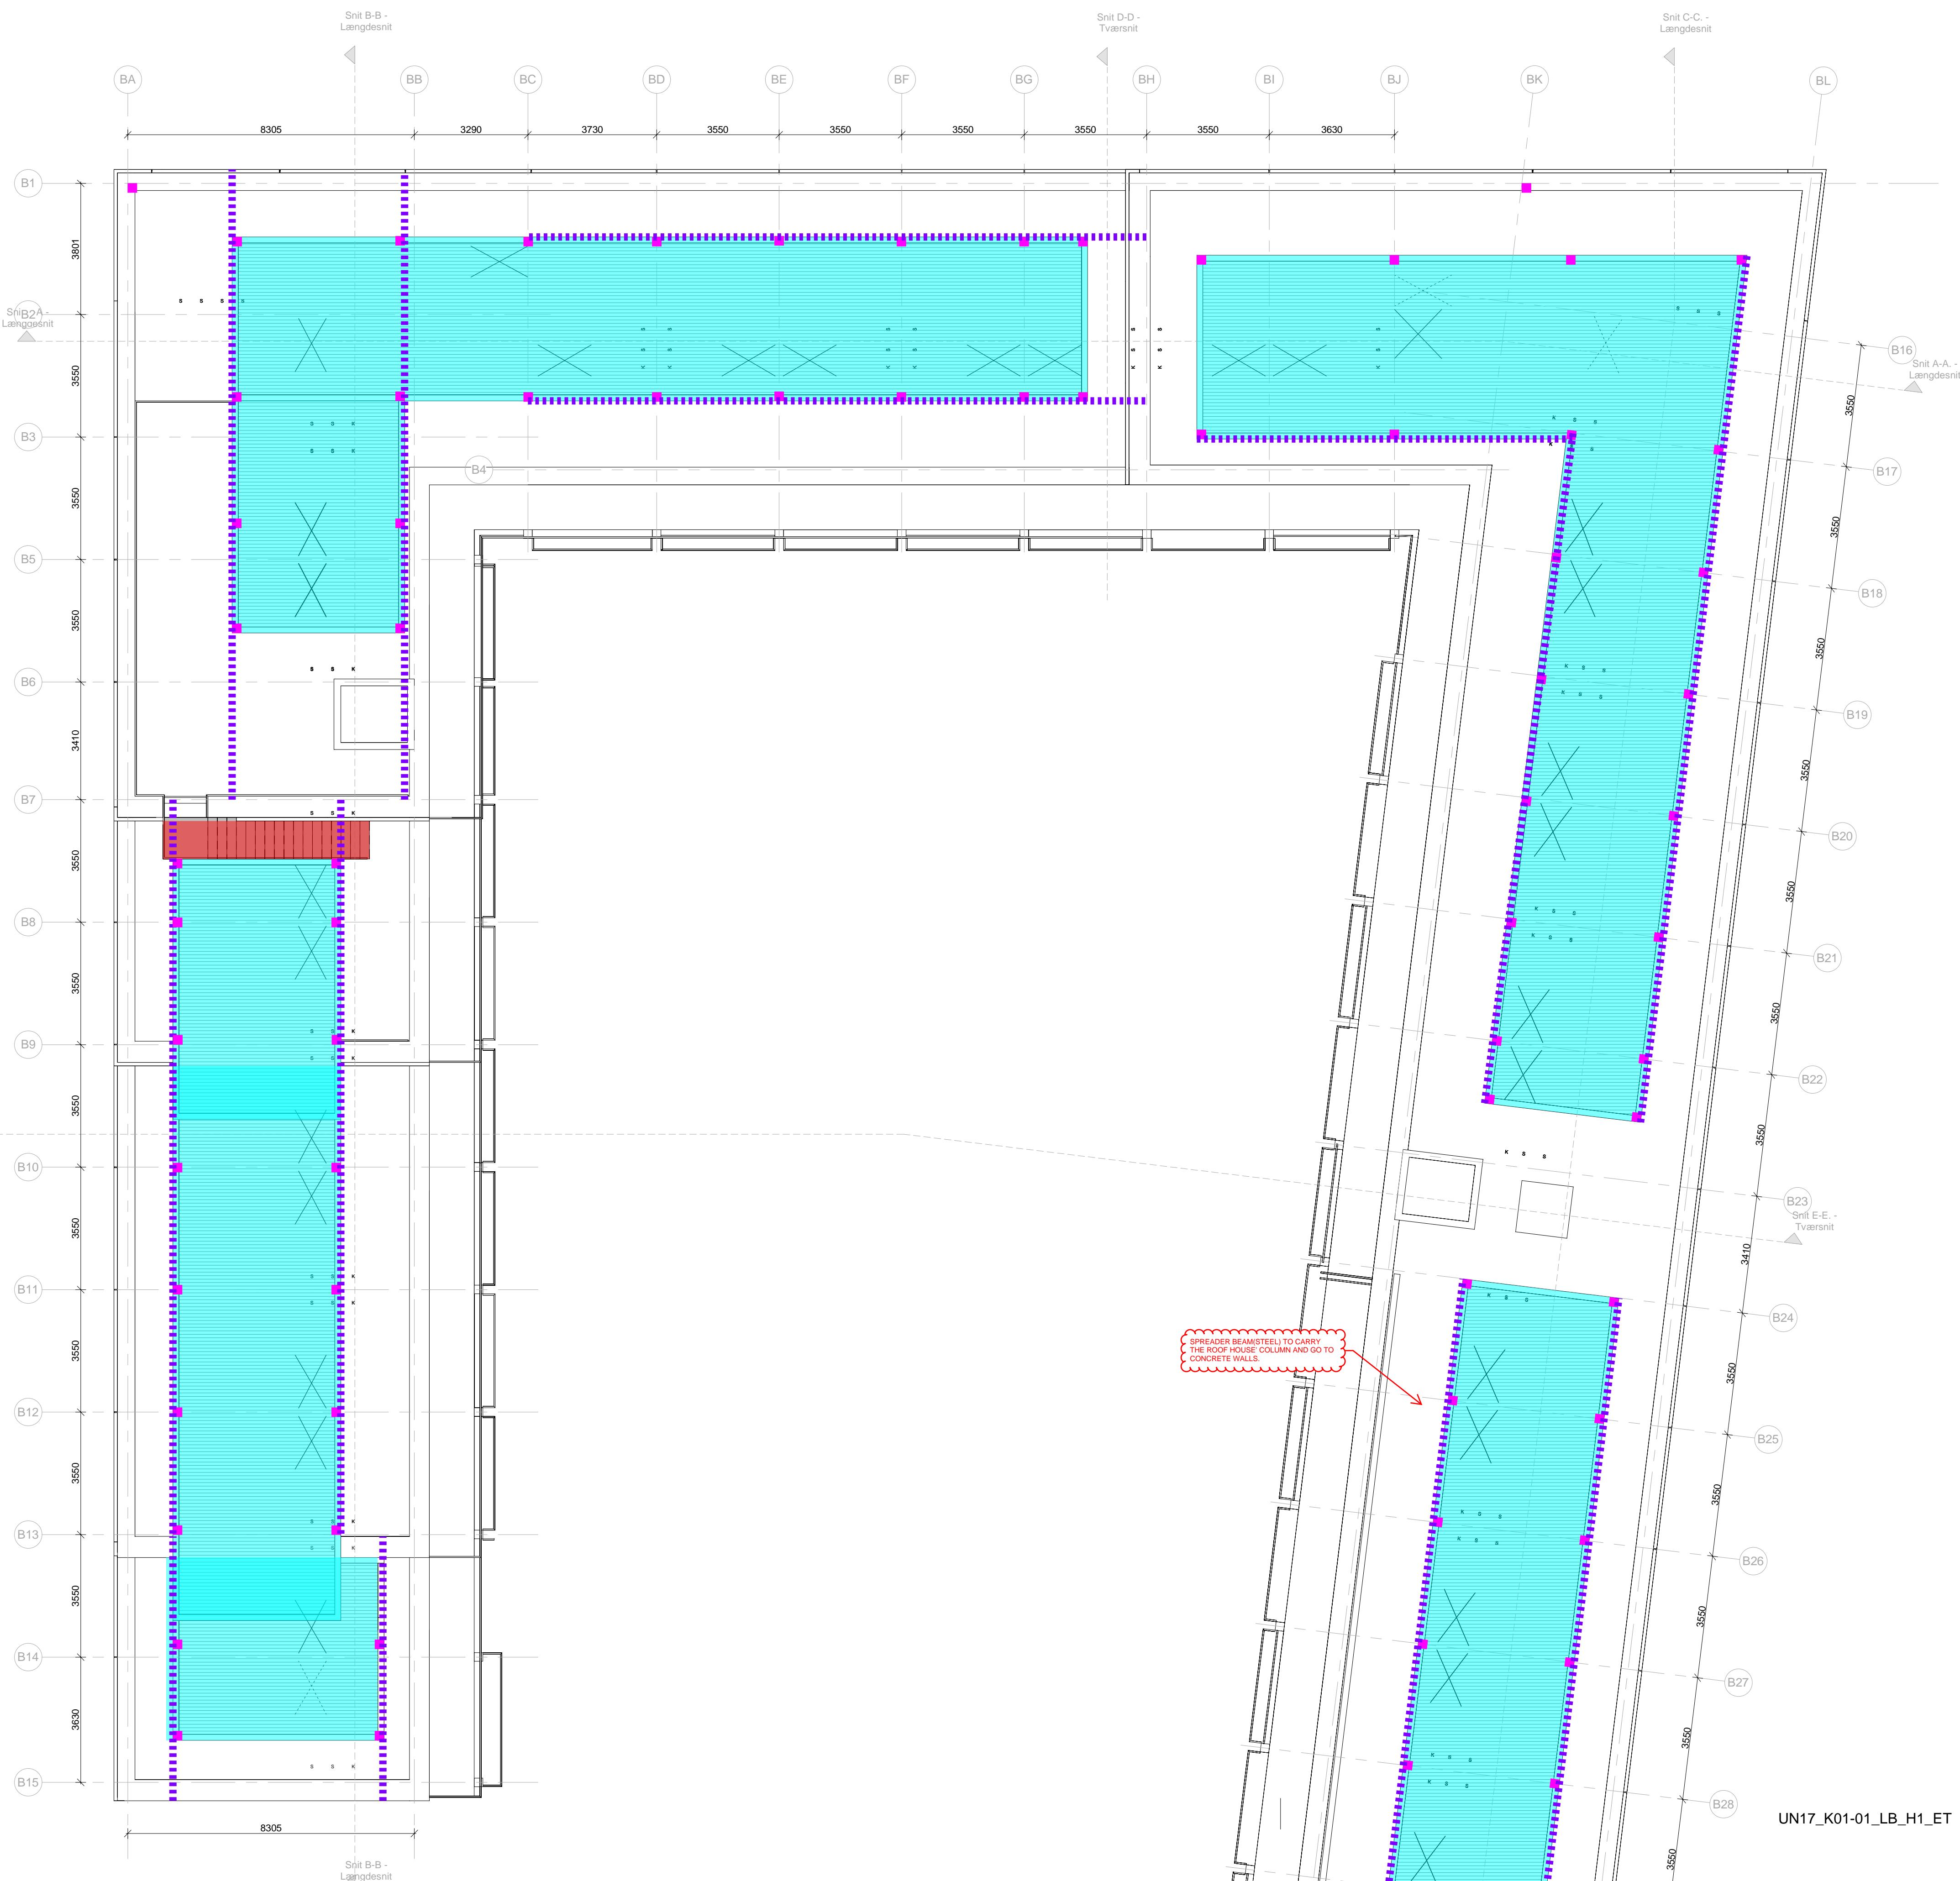

Structural elements for the roof houses are not yet determined.
Proposed columns bearing on roof decks.

Foreløbigt tryk
19-10-2020
13:34:59

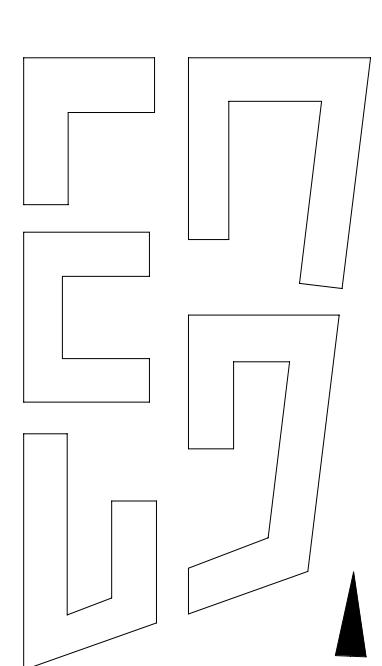

UN17 Village

Bygherre: NREP

Emne: Tagplan

Fase: Projektforslag

Mål: 1 : 100

Sag. nr: 118.6863

Sign: SRM

Ørestads Blvd. 41

2300 København S

T: +45 7024 2100

Dato: 14.05.2020

www.aarstiderne.dk

■ Arkitekt: AARSTIDERNE ARKITEKTER part of Sweco

■ Arkitekt 2: LENDAGER GROUP

■ Ingenier: MOE ARCTELIA GROUP

Buddingevej 272

2680 Søborg

T: +45 44576000

www.moe.dk

TAG

